



PLANO DIRETOR MUNICIPAL

Extrato da Planta de Ordenamento

LEGENDA

-  Limite do Concelho
-  Limite do PDMC
-  U1 UDPG 1 Cidade de Caldas da Rainha
(ver planta 1:10 000)
-  U2 UDPG 2 Salir do Porto
-  U3 UDPG 3 Foz do Arelho
-  U4 UDPG 4 Área de Integração do Nadadouro
-  U5 UDPG 5 Lugar Conjunto do Nadadouro
-  U9 UDPG 9 Área de Equipamento de Apoio Náutico da Foz do Arelho

ESPAÇOS URBANOS

-  Espaço Urbano de Nível 2
-  Espaço Urbano de Nível 3

ESPAÇOS URBANIZÁVEIS

-  Espaços Urbanizáveis de Nível 2
-  Espaço Urbanizável de Turismo

ESPAÇOS DE ENQUADRAMENTO E PROTECÇÃO

-  Área Verde de Enquadramento de nível 2

ESPAÇOS INDUSTRIAIS

-  Áreas Industriais Existentes
-  Áreas Industriais Propostas
-  Áreas de Pequena Indústria

ESPAÇOS DE INDÚSTRIA EXTRACTIVA

-  Espaços de Indústria Extractiva

ESPAÇOS AGRÍCOLAS

-  Áreas Agrícolas
-  Áreas Agro-florestais
-  Áreas de Edificação Dispersa

ESPAÇOS FLORESTAIS

-  Espaços Florestais

ESPAÇOS NATURAIS

-  Áreas Naturais
-  Área do Paúl da Tornada
-  Área de Protecção ao Paúl da Tornada

ESPAÇOS CANAIS

Rodovias Existentes/Propostas

-  Itinerário Principal (A15)
-  Itinerário Complementar (A8)
-  Estrada Nacional
-  Estrada a Desclassificar
-  Estrada/Caminho Municipal

Rede Eléctrica Existentes/Propostas

-  Linhas de Muito Alta Tensão

Ferrovias

- 

Nota: Os espaços Urbanos, os espaços Urbanizáveis e as Áreas Verdes de Enquadramento, de nível 1 são representados na planta 1:10 000






PLANO DIRETOR MUNICIPAL

Extrato da Planta de Condicionantes



Escala: 1:25000

Requerente:
Freguesia: Nadadouro
Lugar: Nadadouro

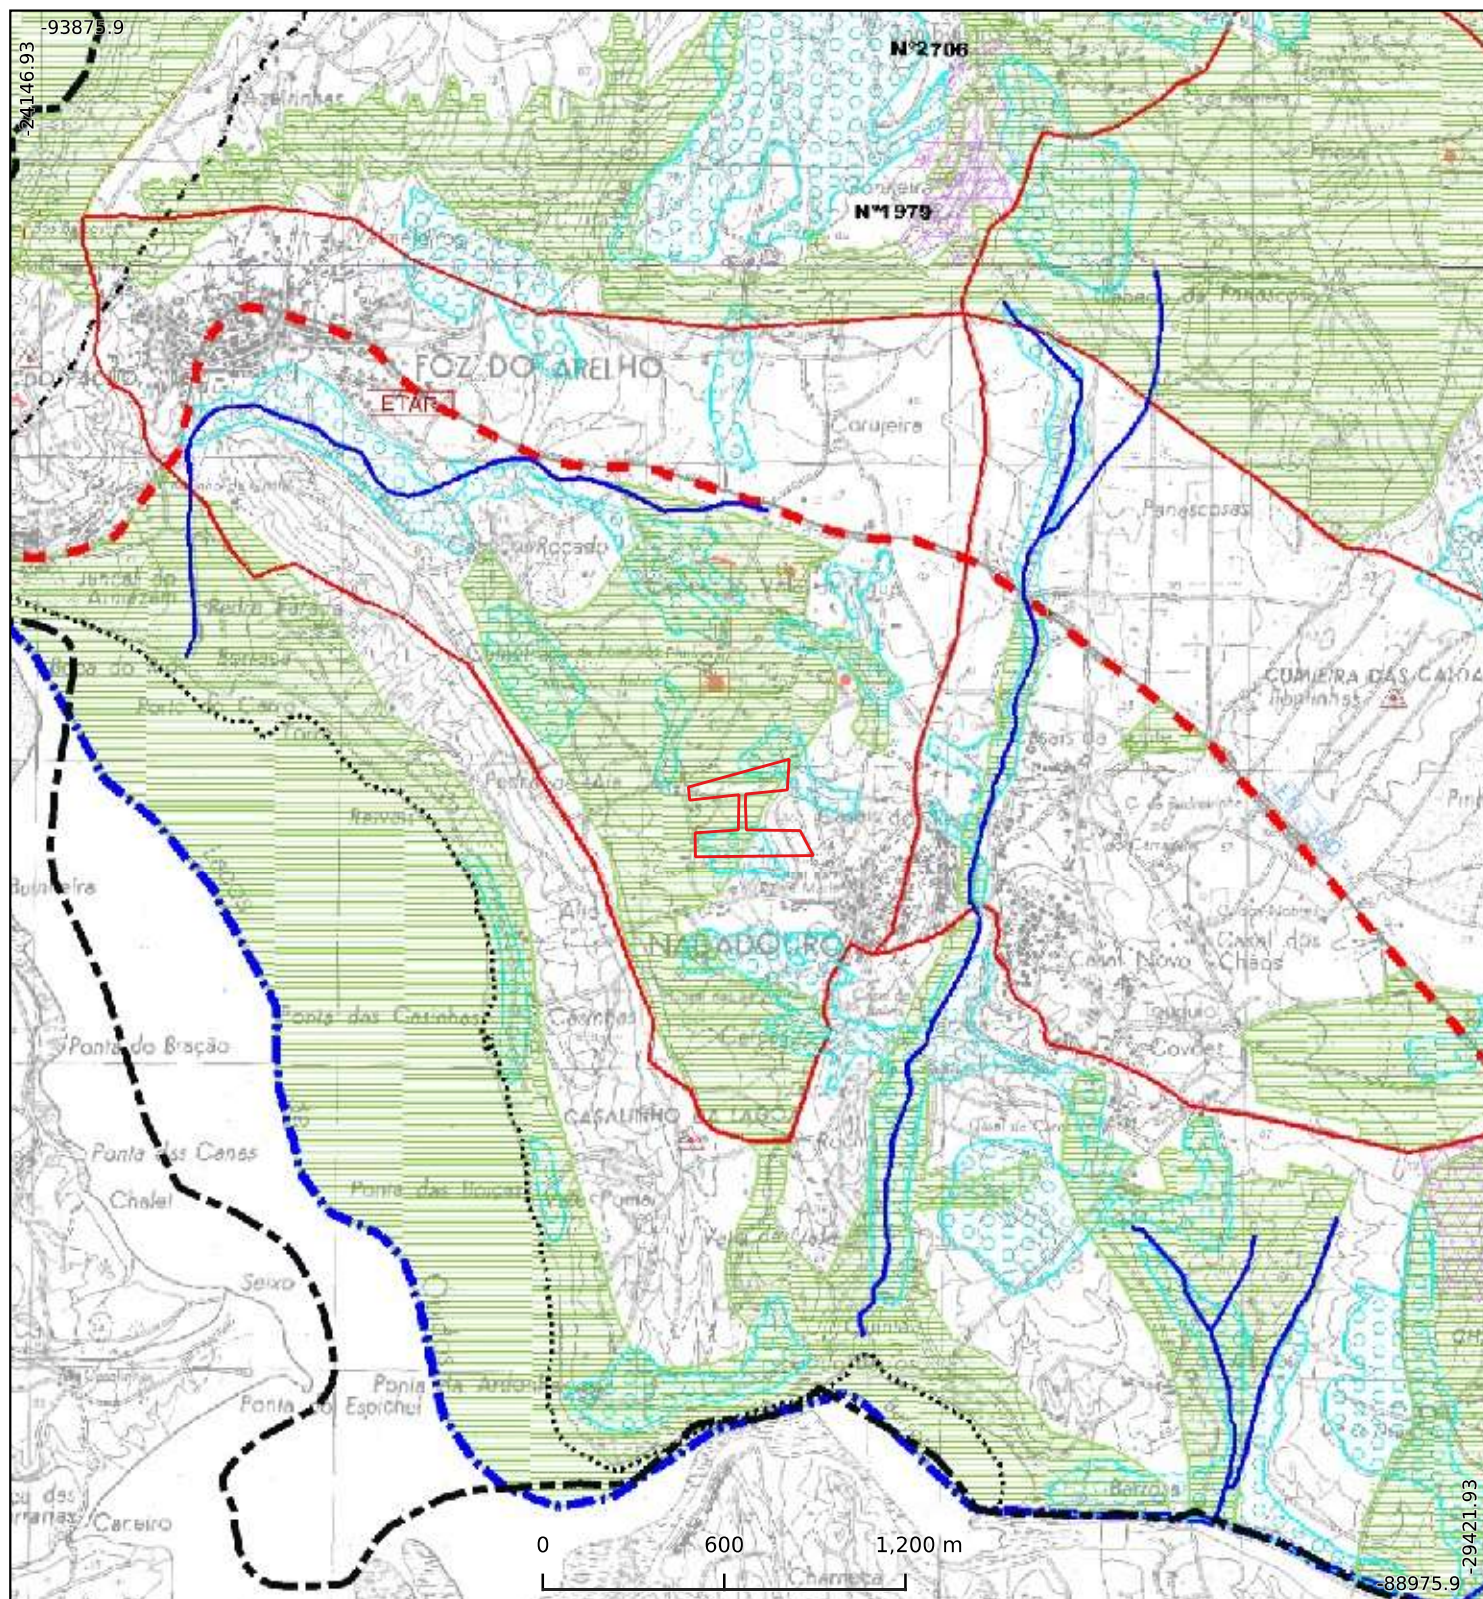

Fonte: PDM de Caldas da Rainha (Resolução Conselho Ministros n.º 101/2002 / DR I Série B n.º 138, 18 de junho de 2002 e subsequentes alterações)
Não dispensa a consulta dos elementos publicados em Diário da República e disponíveis na página eletrónica da DGT.
Sistema de referência: PT - TM06/ETRS89

Data 13-01-2026 Funcionário _____ | ID 10842

Nota: A identificação da localização e marcação do polígono são da inteira responsabilidade do requerente.



LEGENDA





CARTOGRAFIA

Extrato de Ortofotomapa

Requerente:
Freguesia: Nadadouro
Lugar: Nadadouro



Escala: 1:5000



Fonte: Ortocartografia do Município de Caldas da Rainha à escala 1:2 000 Resolução 0.10 m (2017).
Sistema de referência: PT - TM06/ETRS89

Data 13-01-2026 Funcionário _____ | ID 10841

Área: 25706.9 m²

Nota: A identificação da localização e marcação do polígono são da inteira responsabilidade do requerente.




CARTOGRAFIA

Extrato de Cartografia Vetorial

Requerente:
Freguesia: Nadadouro
Lugar: Nadadouro



Escala: 1:5000

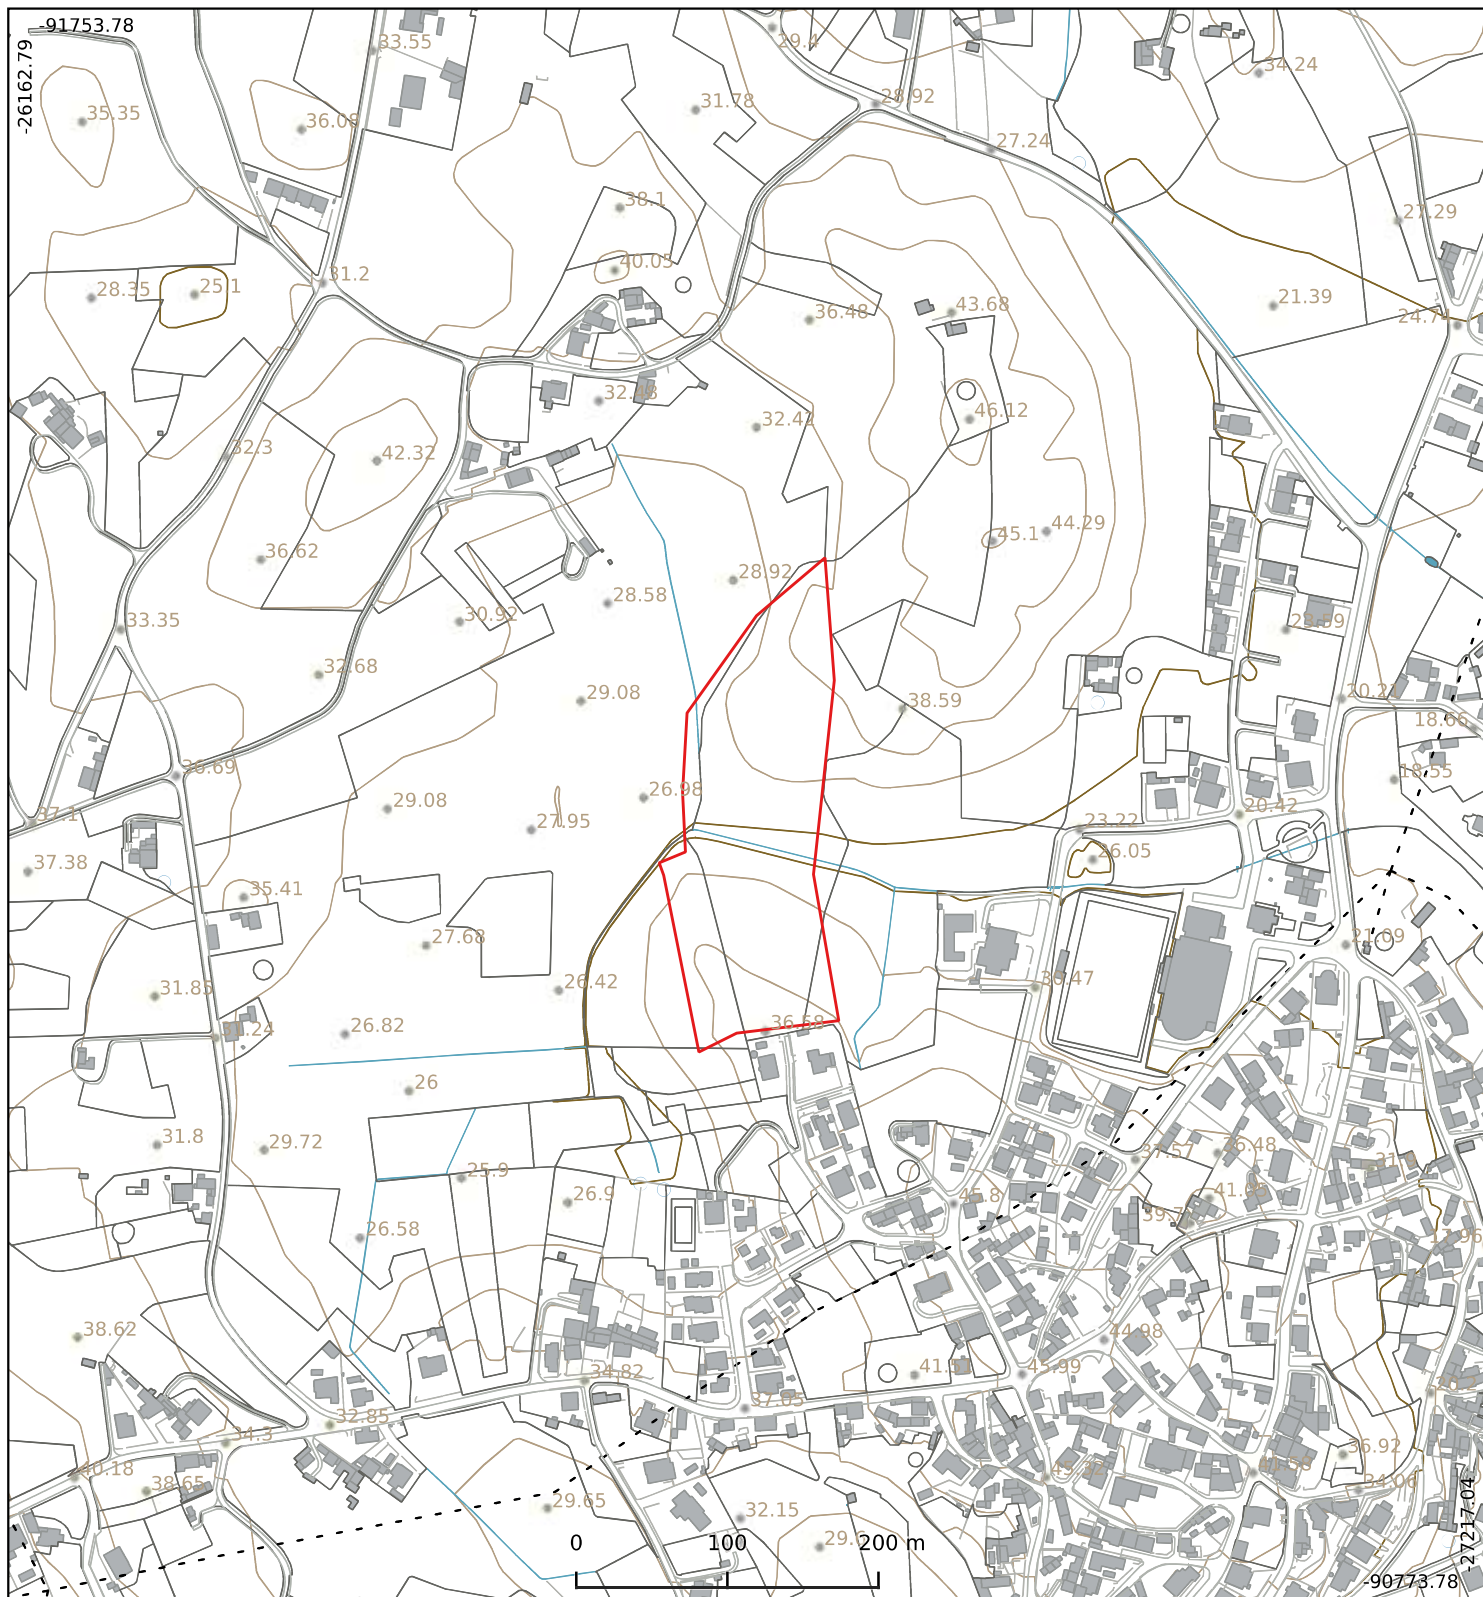

Fonte: Município de Caldas da Rainha | Cartografia vetorial do Município de Caldas da Rainha à escala 1:10 000 (2018).
Sistema de referência: PT - TM06/ETRS89

Data 13-01-2026 Funcionário _____ | ID 10841


Nota: A identificação da localização e marcação do polígono são da inteira responsabilidade do requerente.

Extrato da Carta Militar de Portugal



Escala: 1:25000

Requerente:
Freguesia: Nadadouro
Lugar: Nadadouro

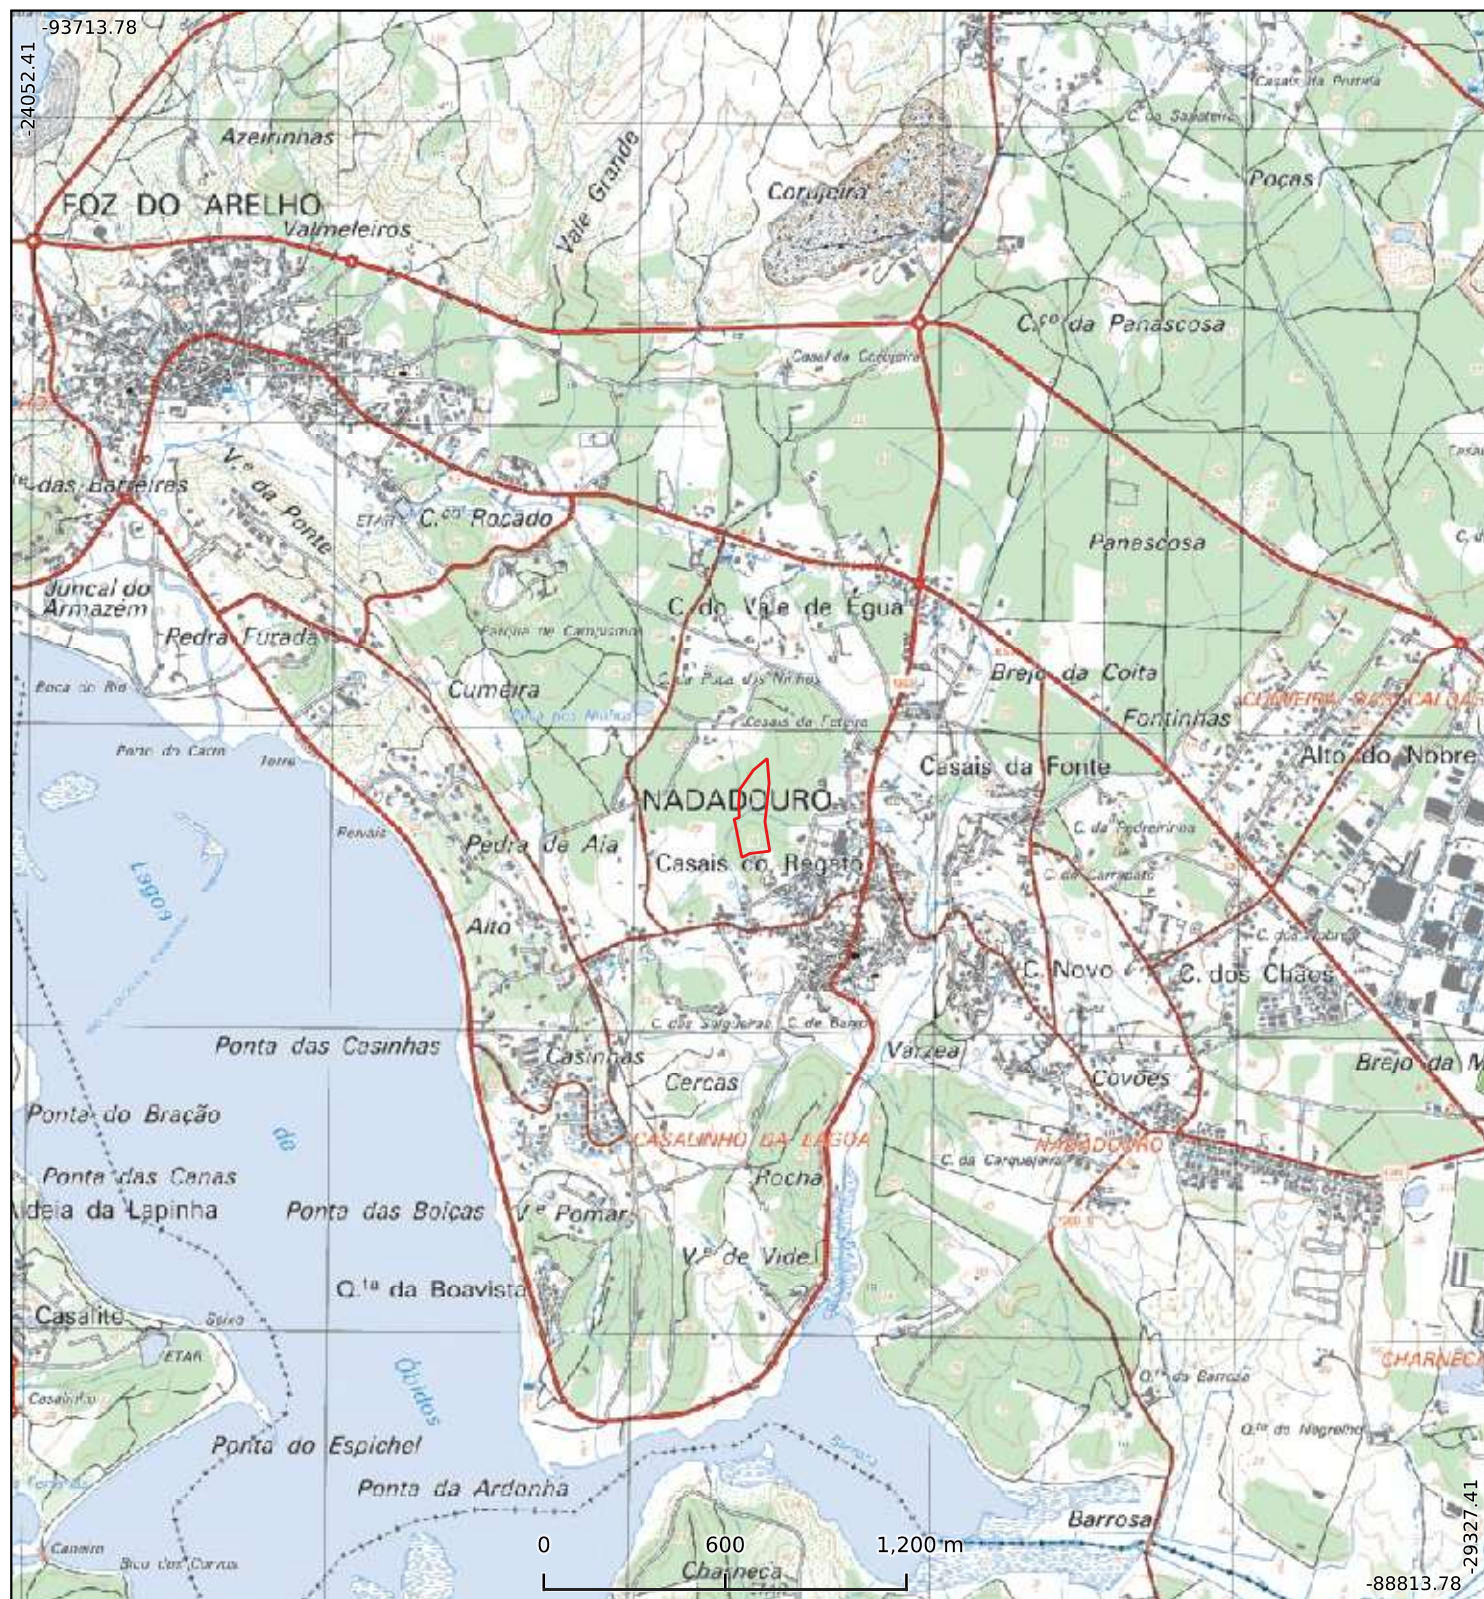

Fonte: Centro de Informação Geoespacial do Exército | Carta Militar à escala 1:25 000 Série M888 (2014).
Sistema de referência: PT - TM06/ETRS89




PLANO DIRETOR MUNICIPAL

Extrato da Planta de Ordenamento



Escala: 1:25000

Requerente:
Freguesia: Nadadouro
Lugar: Nadadouro

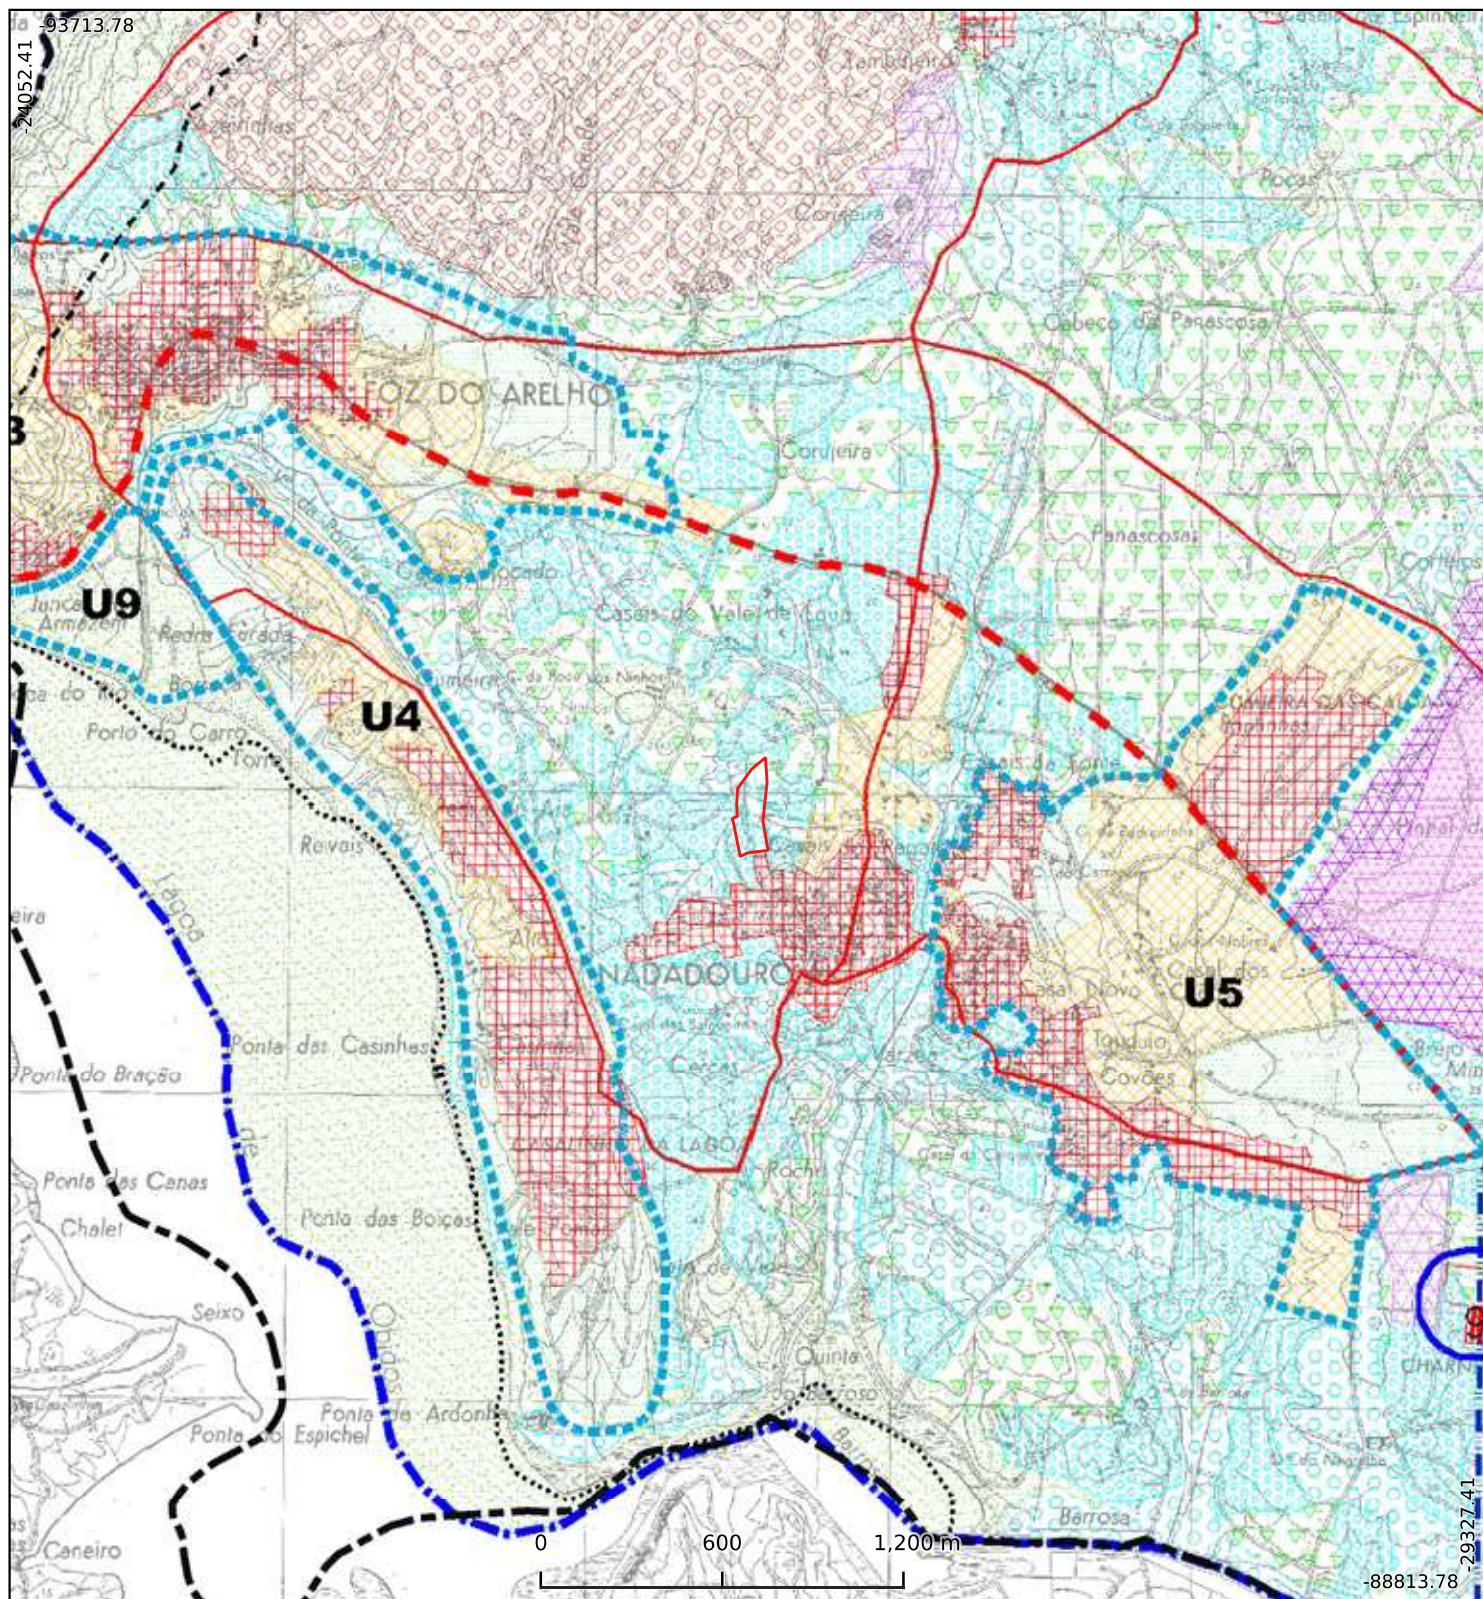

Fonte: PDM de Caldas da Rainha (Resolução Conselho Ministros n.º 101/2002 / DR I Série B n.º 138, 18 de junho de 2002 e subsequentes alterações)
Não dispensa a consulta dos elementos publicados em Diário da República e disponíveis na página eletrónica da DGT.
Sistema de referência: PT - TM06/ETRS89

Data 13-01-2026 Funcionário _____ | ID 10841

Nota: A identificação da localização e marcação do polígono são da inteira responsabilidade do requerente.



PLANO DIRETOR MUNICIPAL

Extrato da Planta de Ordenamento

LEGENDA

-  Limite do Concelho
-  Limite do PDMC
-  U1 UDPG 1 Cidade de Caldas da Rainha
(ver planta 1:10 000)
-  U2 UDPG 2 Salir do Porto
-  U3 UDPG 3 Foz do Arelho
-  U4 UDPG 4 Área de Integração do Nadadouro
-  U5 UDPG 5 Lugar Conjunto do Nadadouro
-  U9 UDPG 9 Área de Equipamento de Apoio Náutico da Foz do Arelho

ESPAÇOS URBANOS

-  Espaço Urbano de Nível 2
-  Espaço Urbano de Nível 3

ESPAÇOS URBANIZÁVEIS

-  Espaços Urbanizáveis de Nível 2
-  Espaço Urbanizável de Turismo

ESPAÇOS DE ENQUADRAMENTO E PROTECÇÃO

-  Área Verde de Enquadramento de nível 2

ESPAÇOS INDUSTRIAIS

-  Áreas Industriais Existentes
-  Áreas Industriais Propostas
-  Áreas de Pequena Indústria

ESPAÇOS DE INDÚSTRIA EXTRACTIVA

-  Espaços de Indústria Extractiva

ESPAÇOS AGRÍCOLAS

-  Áreas Agrícolas
-  Áreas Agro-florestais
-  Áreas de Edificação Dispersa

ESPAÇOS FLORESTAIS

-  Espaços Florestais

ESPAÇOS NATURAIS

-  Áreas Naturais
-  Área do Paúl da Tornada
-  Área de Protecção ao Paúl da Tornada

ESPAÇOS CANAIS

Rodovias Existentes/Propostas

-  Itinerário Principal (A15)
-  Itinerário Complementar (A8)
-  Estrada Nacional
-  Estrada a Desclassificar
-  Estrada/Caminho Municipal

Rede Eléctrica Existentes/Propostas

-  Linhas de Muito Alta Tensão

Ferrovias

- 

Nota: Os espaços Urbanos, os espaços Urbanizáveis e as Áreas Verdes de Enquadramento, de nível 1 são representados na planta 1:10 000






PLANO DIRETOR MUNICIPAL

Extrato da Planta de Condicionantes



Escala: 1:25000

Requerente:
Freguesia: Nadadouro
Lugar: Nadadouro

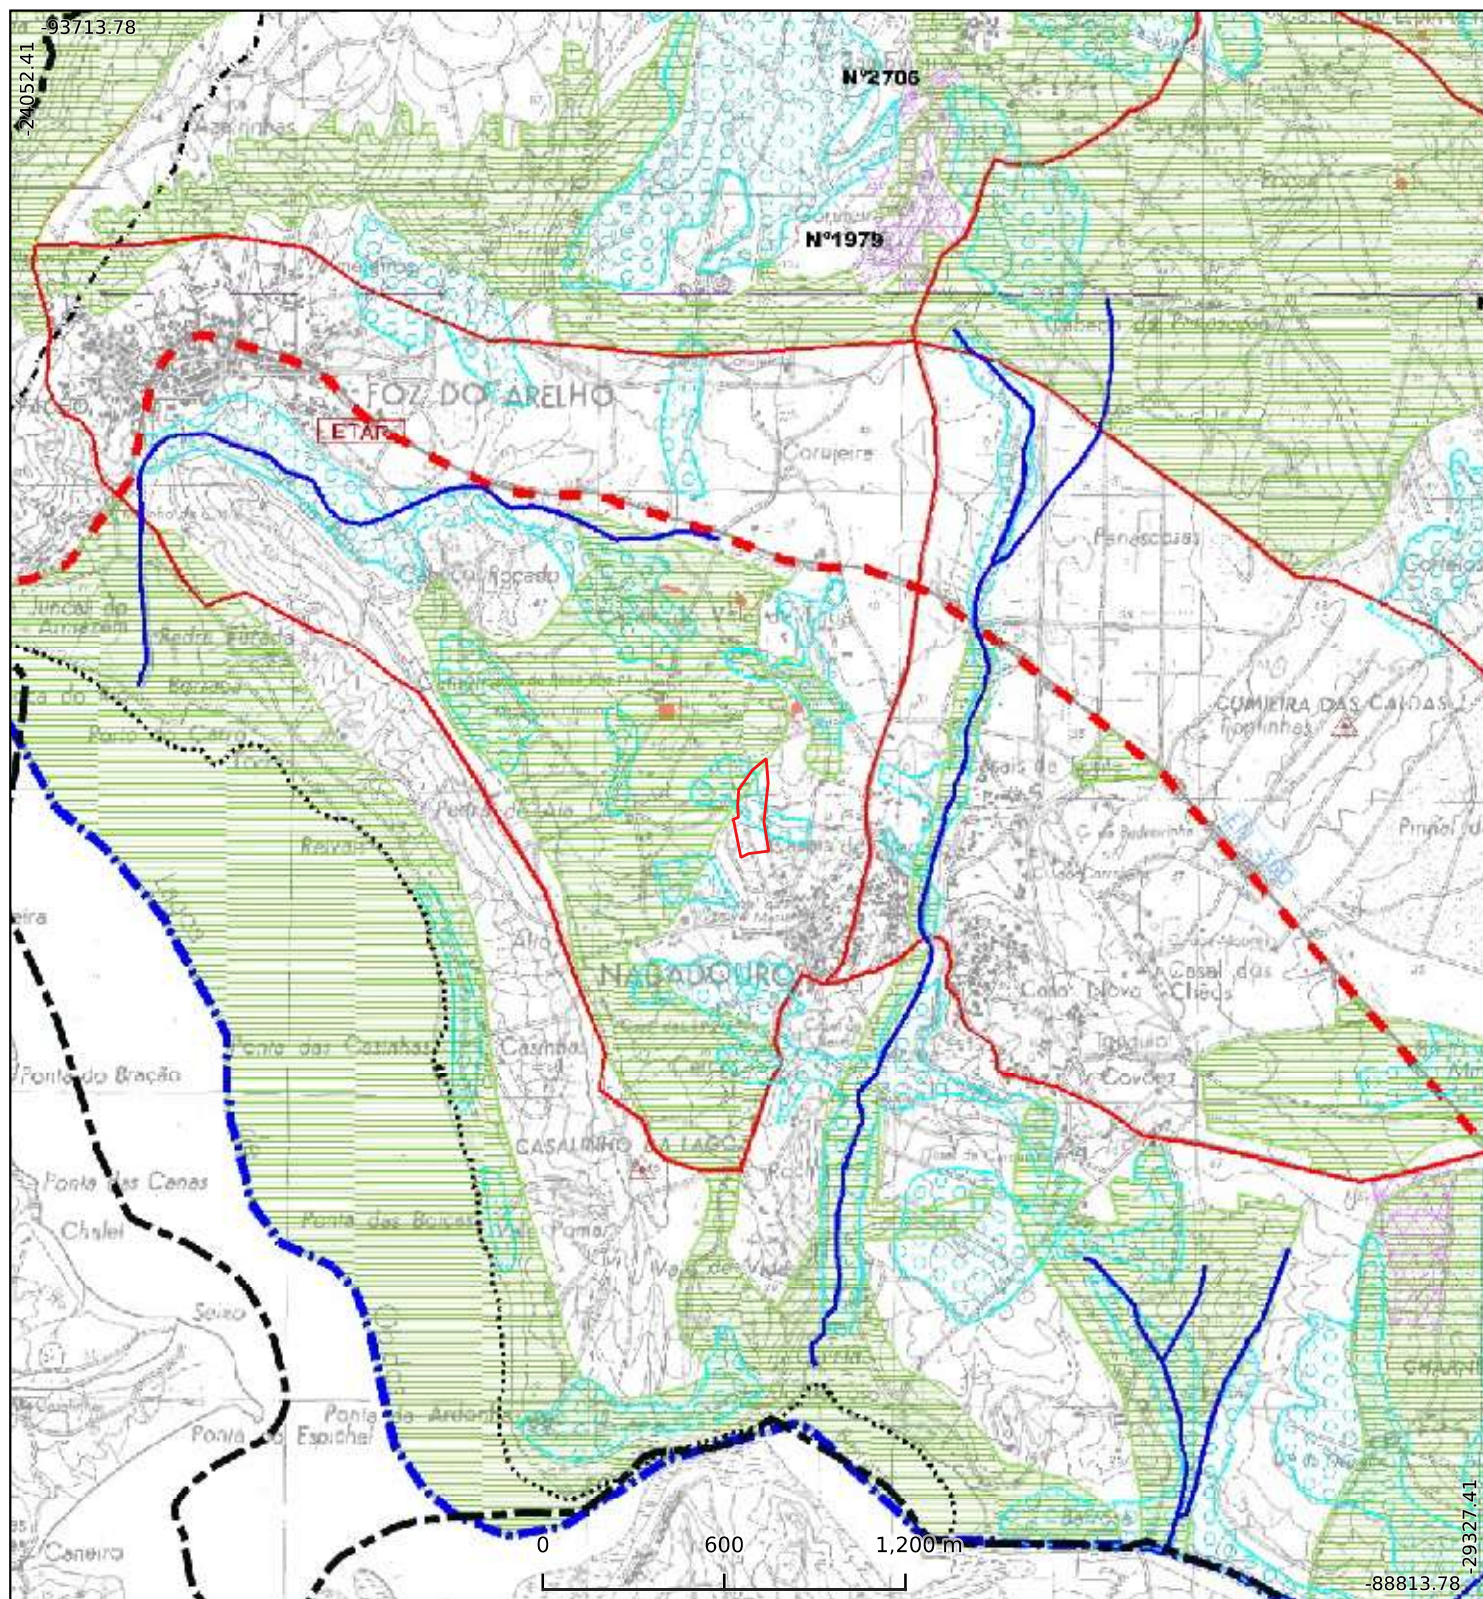

Fonte: PDM de Caldas da Rainha (Resolução Conselho Ministros n.º 101/2002 / DR I Série B n.º 138, 18 de junho de 2002 e subsequentes alterações)
Não dispensa a consulta dos elementos publicados em Diário da República e disponíveis na página eletrónica da DGT.
Sistema de referência: PT - TM06/ETRS89

Data 13-01-2026 Funcionário _____ | ID 10841

Nota: A identificação da localização e marcação do polígono são da inteira responsabilidade do requerente.



LEGENDA

0 1 Km


As linhas da quadricula referem-se à Quadricula Principal Quilométrica (1:134.500,28). Escala: 1:134.500,28.



Cliente
 Norbert Roztocki
 Untere Roostmatt 8
 6300 Zug - Suíça
 Projectista
 Arq.º João Jorge
 a011005703.reg.ucc1-308@remi.live
 Nev Freeman®

Uso	Função	ABC total (m²)	ABC relevante para índice/ uso turístico (m²)	Nº unidades
Turismo	Quartos duplos	321.97	321.97	10
Turismo	Áreas comuns	227.85	227.85	—
Serviço	Apoios hotel	50.18	50.18	—
Técnico	Estacionamento em cave	341.73	0	—
Técnico	Áreas técnicas em cave	60.26	0	—
Agroflorestal	Cavalariças	68	0	—
Agroflorestal	Armazém / laboratório	96	0	—
Agroflorestal	Estufa agrícola	-	-	-
Total		1166	600	

- Legenda Geral
 - Caminhos acesso
 - Caminhos pedonais
 - Estacionamento exterior
 - Zonas verdes
 - Piscina
 - Cobertura Ajudinada
 - Implantação Apoios Agro-florestal

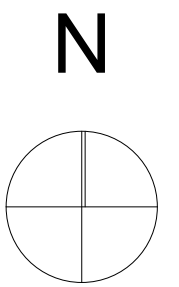

PROJEITO
 Hotel Rural com Apoios à Exploração Agroflorestal
 LOCAL
 Nadadouro, Caldas da Rainha
 FASE
 Pedido de Informação Prévia
 DATA
 27/01/2026
 ESCALA
 1:200
 TÍTULO
 Planta de Coberturas, Levantamento topográfico


DESENHO Nº
 A.01.4
 FICHEIRO
 EP_2025_04_A_NORBERT_NADADOURO_3.ph



Cliente
Norbert Roztocki
Untere Roostmatt 8
6300 Zug - Suíça

Projectista
Arq.º João Jorge
a011005703.reg.ucc1-308@reml.live
Nev Freeman®

- Legenda Acessibilidades**
- Caminhos acesso
 - Caminhos pedonais
 - Estacionamento exterior
 - Zonas verdes
 - Piscina
 - Implantação Hotel
 - Implantação Estacionamento coberto
 - Implantação Apoios Agro-florestal
 - Rede Acessível de acesso aos edifícios

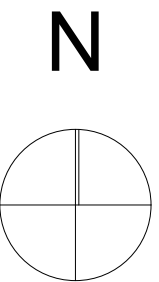

Hotel Rural com Apoios à Exploração Agroflorestal

Nadadouro, Caldas da Rainha

Pedido de Informação Prévia

27/01/2026

1:500

Planta de Acessibilidades - Rede Acessível, Levantamento topográfico

A.01.6

DESENHO Nº

FICHEIRO

EP_2025_04_A_NORBERT_NADADOURO_3.pln




Cliente
Norbert Roztocki
Untere Roostmatt 8
6300 Zug - Suíça

Projectista
Arq.º João Jorge
a011005703.reg.ucc1-308@remi.live
Nev Freeman®

Uso	Função	ABC total (m²)	ABC relevante para índice/ uso turístico (m²)	Nº unidades
Turismo	Quartos duplos	321.97	321.97	10
Turismo	Áreas comuns	227.85	227.85	—
Serviço	Apoios hotel	50.18	50.18	—
Técnico	Estacionamento em cave	341.73	0	—
Técnico	Áreas técnicas em cave	60.26	0	—
Agroflorestal	Cavalaças	68	0	—
Agroflorestal	Armazém / laboratório	96	0	—
Agroflorestal	Estufa agrícola	-	-	-
Total		1166	600	

- Legenda Geral
- Caminhos acesso
 - Caminhos pedonais
 - Estacionamento exterior
 - Zonas verdes
 - Piscina
 - Cobertura Ajardinada
 - Implantação Apoios Agro-florestal

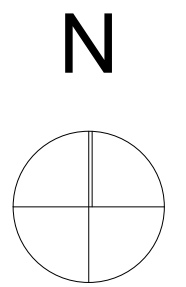

PROJETO
Hotel Rural com Apoios à Exploração Agroflorestal

LOCAL
Nadadouro, Caldas da Rainha

FASE
Pedido de Informação Prévia


DATA
27/01/2026

ESCALA
1:200

TÍTULO
Planta do Rés-do-Chão (piso 0), Levantamento topográfico

DESENHO Nº
A.01.2


FICHEIRO
EP_2025_04_A_NORBERT_NADADOURO_3.plt

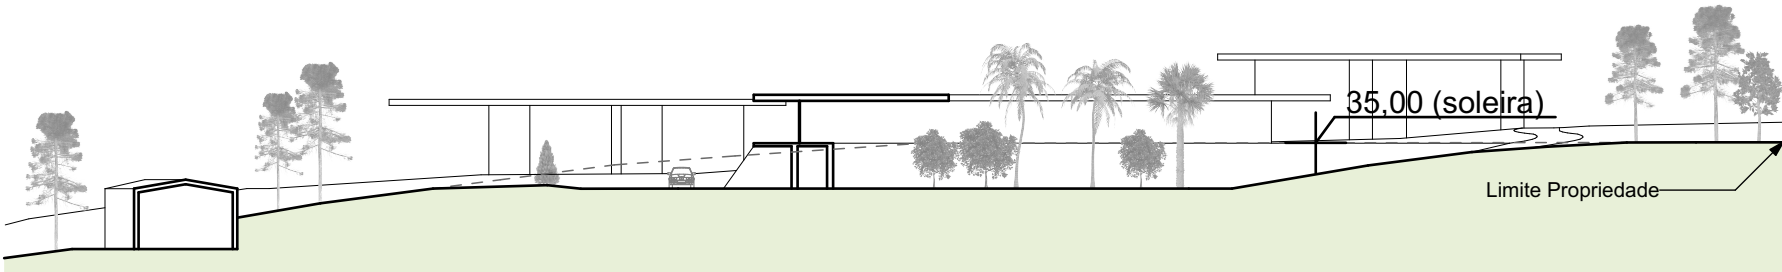

FT-18

Corte Norte-Sul



1:500

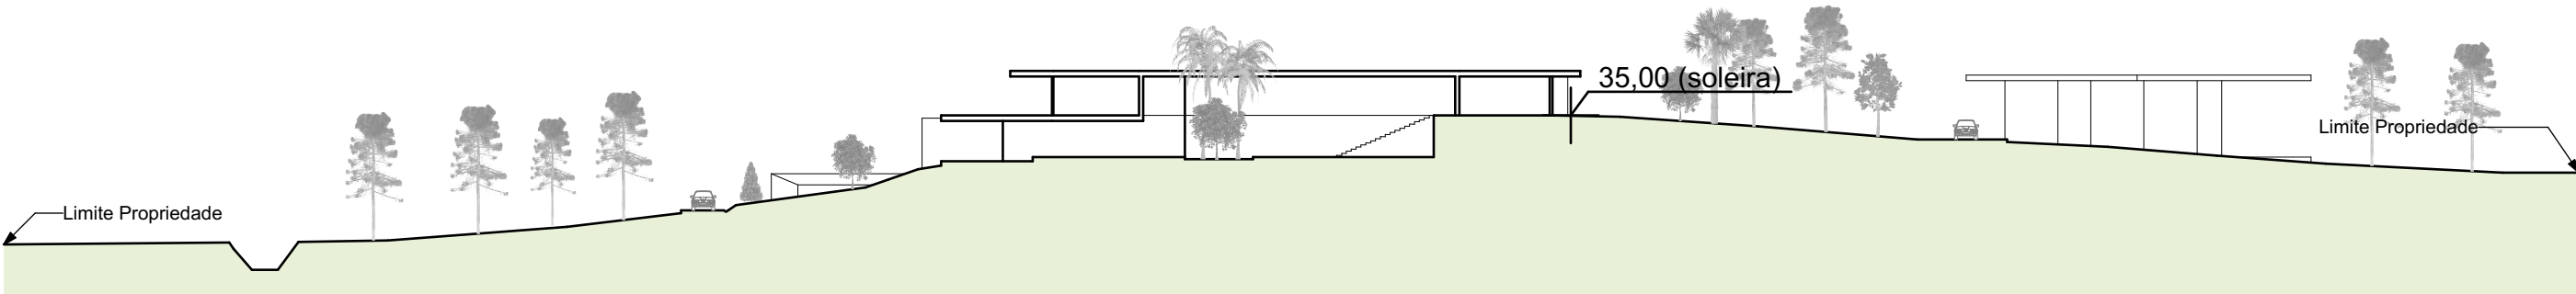

FT-19

Corte Poente-Nascente

1:500

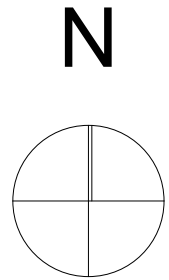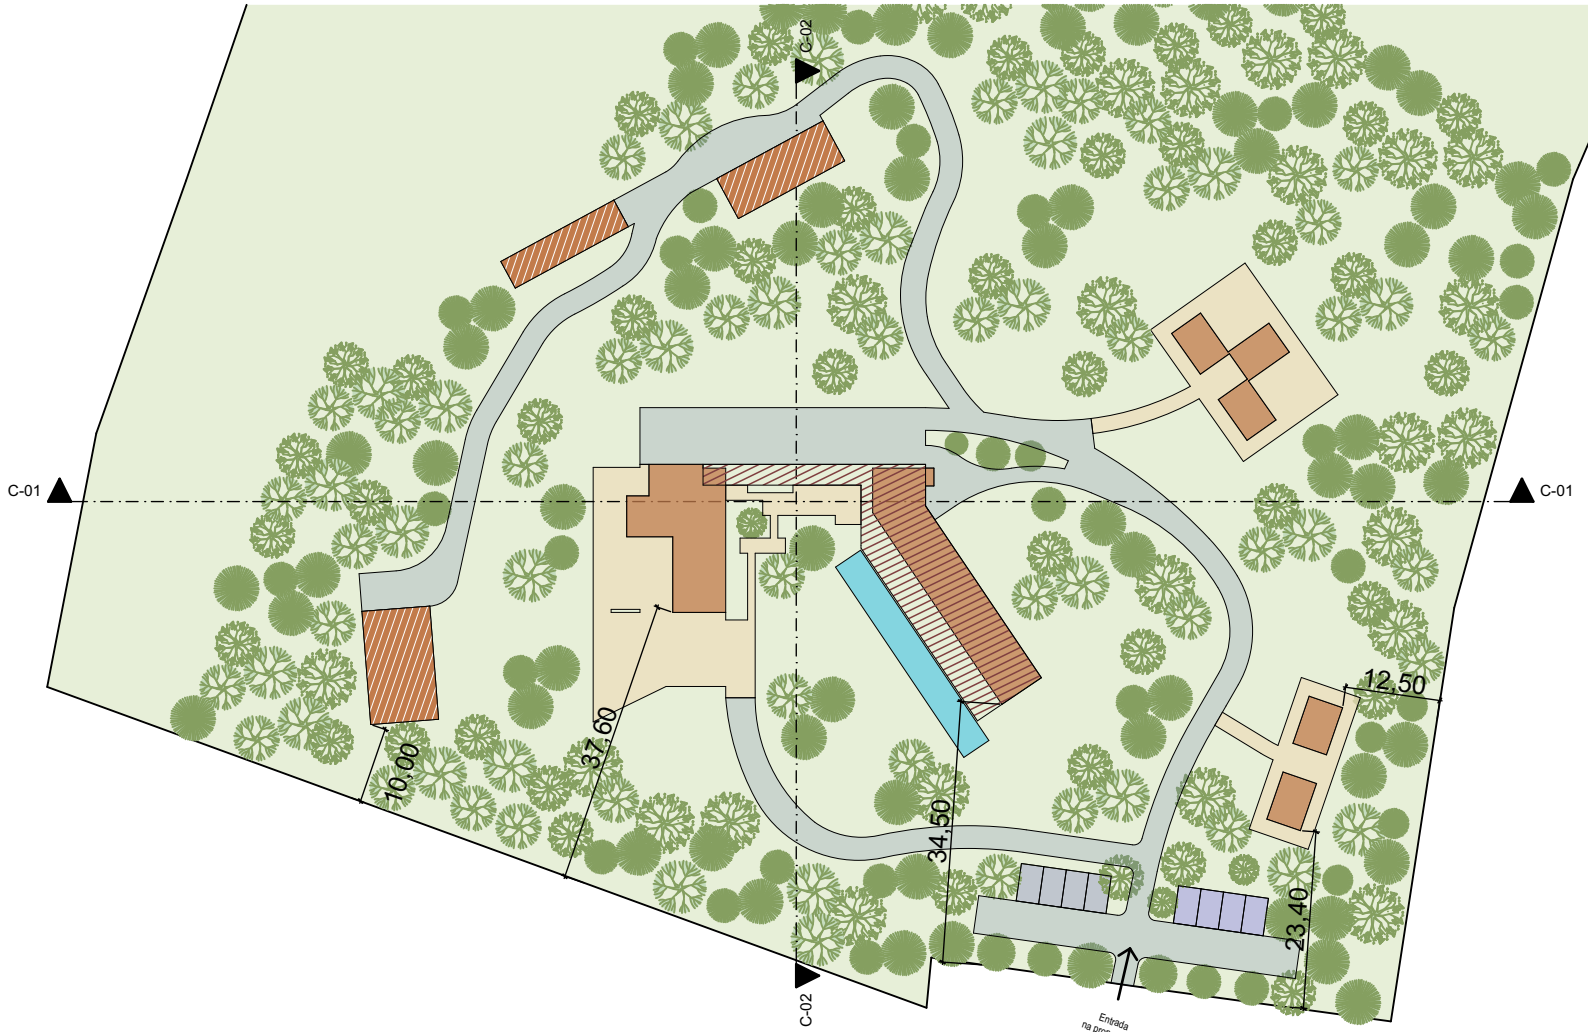

Hotel Rural com Apoios à Exploração Agroflorestal	PROJECTO
Nadadouro, Caldas da Rainha	LOCAL
Pedido de Informação Prévia	FASE
29/01/2026	DATA
1:500, 1:1000	ESCALA
Corte Norte-Sul, Corte Poente-Nascente	TÍTULO
A.01.7	DESENHO Nº
EP_2025_04_A_NORBERT_NADADOURO_3.pln	FICHEIRO