


FT-18

Corte Norte-Sul



1:500

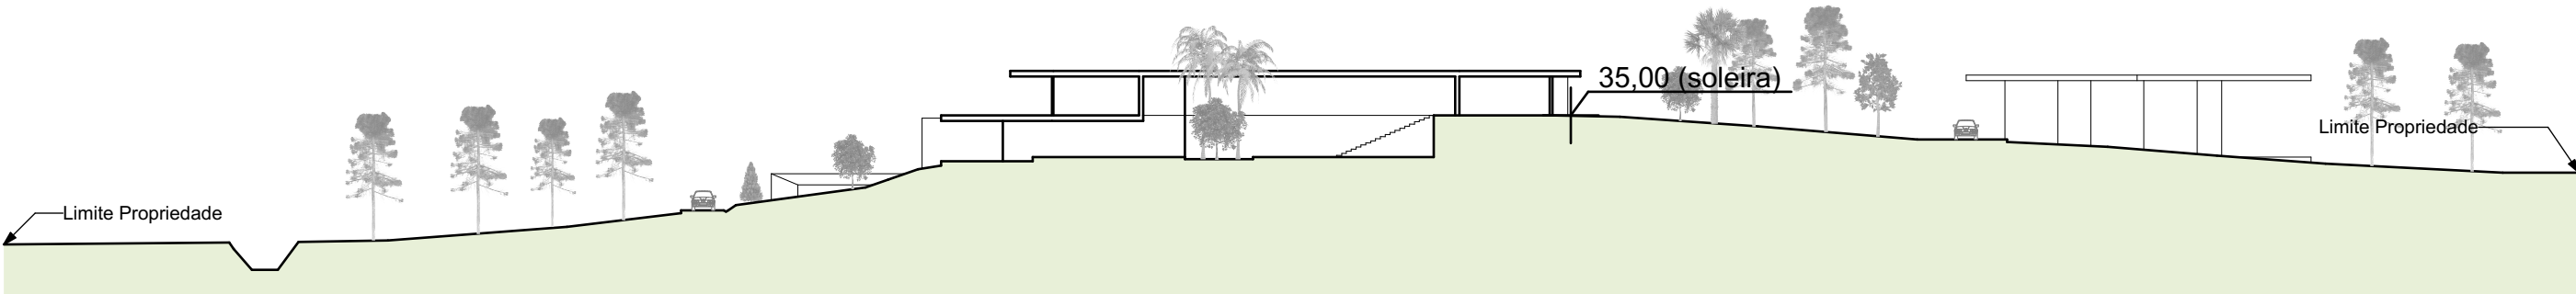

FT-19

Corte Poente-Nascente

1:500

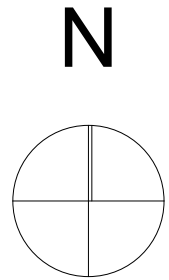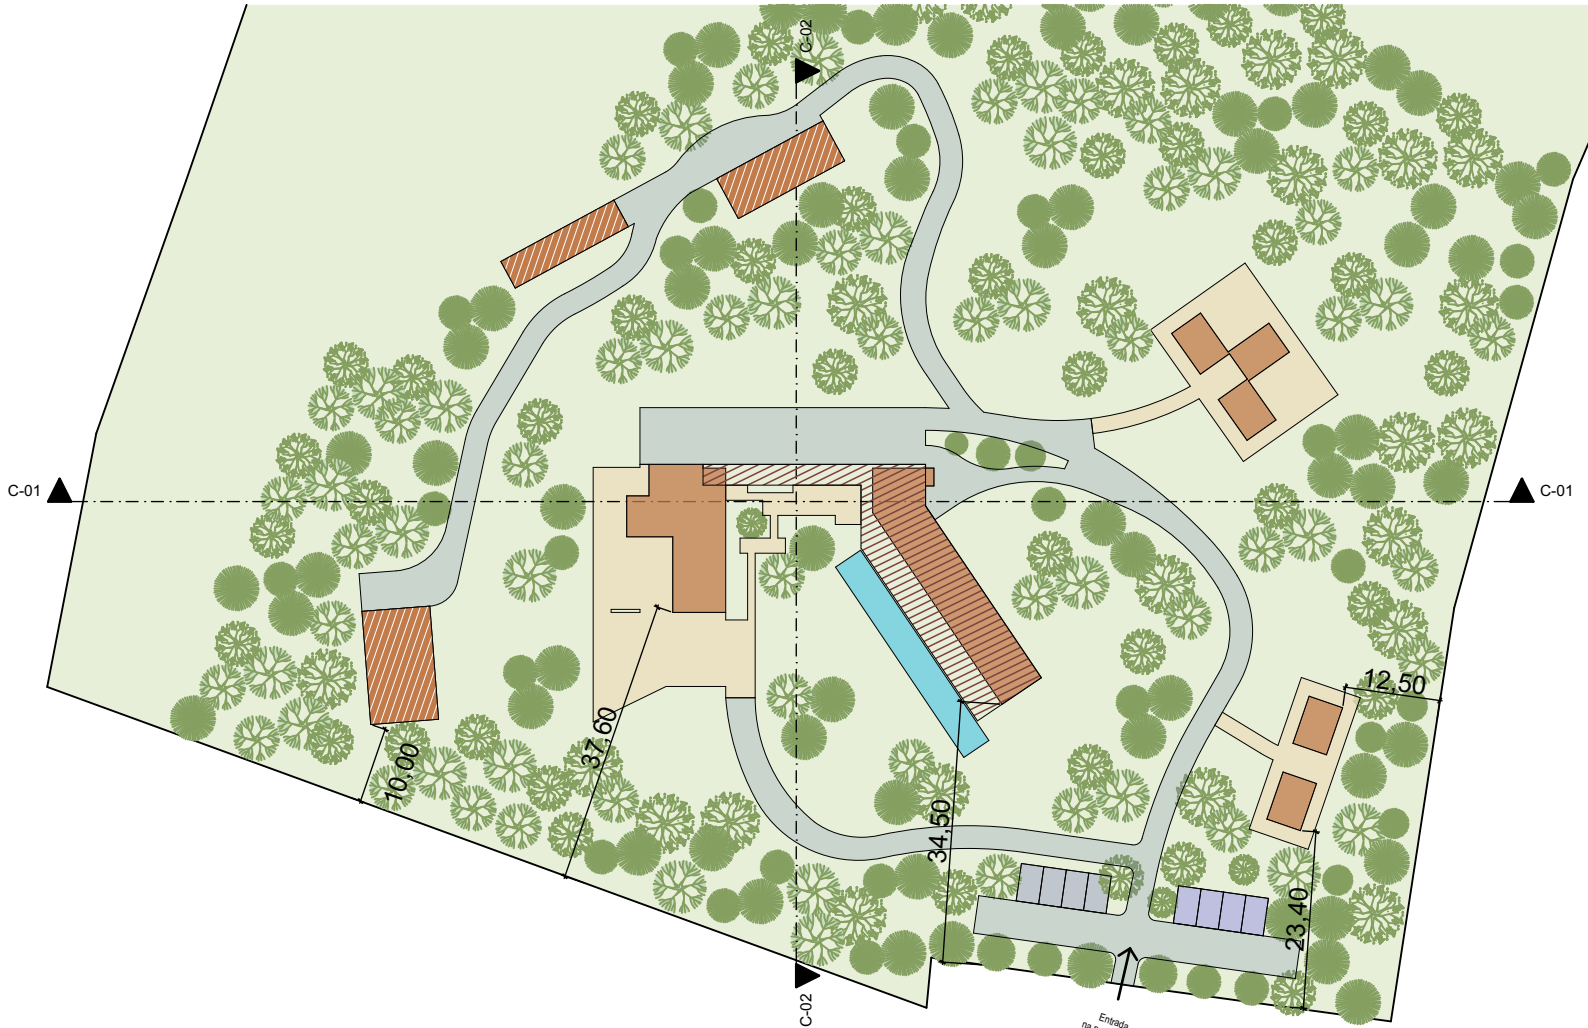

Hotel Rural com Apoios à Exploração Agroflorestal	PROJECTO
Nadadouro, Caldas da Rainha	LOCAL
Pedido de Informação Prévia	FASE
29/01/2026	DATA
1:500, 1:1000	ESCALA
Corte Norte-Sul, Corte Poente-Nascente	TÍTULO
A.01.7	DESENHO Nº
EP_2025_04_A_NORBERT_NADADOURO_3.pln	FICHEIRO



Cliente

Norbert Roztocki
Untere Roostmatt 8
6300 Zug - Suíça


Projectista

Arq.º João Jorge
a011005703.reg.ucc1-308@remi.live
Nev Freeman®

Legenda Infra-estruturas

- Caminhos acesso
- Caminhos pedonais
- Estacionamento exterior
- Zonas verdes
- Piscina
- Implantação Hotel
- Implantação Estacionamento coberto
- Implantação Apoios Agro-florestal
- Ligação infra-estruturas Águas
- Ligação infra-estruturas Redes eléctricas
- Ligação infra-estruturas Rede de esgotos

N

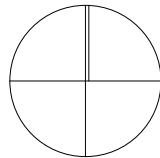

PROJECTO
Hotel Rural com Apoios à Exploração Agroflorestal

LOCAL
Nadadouro, Caldas da Rainha

FASE
Pedido de Informação Prévia

DATA
27/01/2026

ESCALA
1:500


TÍTULO
Ligações infra-estruturas,
Levantamento topográfico

DESENHO Nº

A.01.5

FICHEIRO

EP_2025_04_A_NORBERT_NADADOURO_3.pln

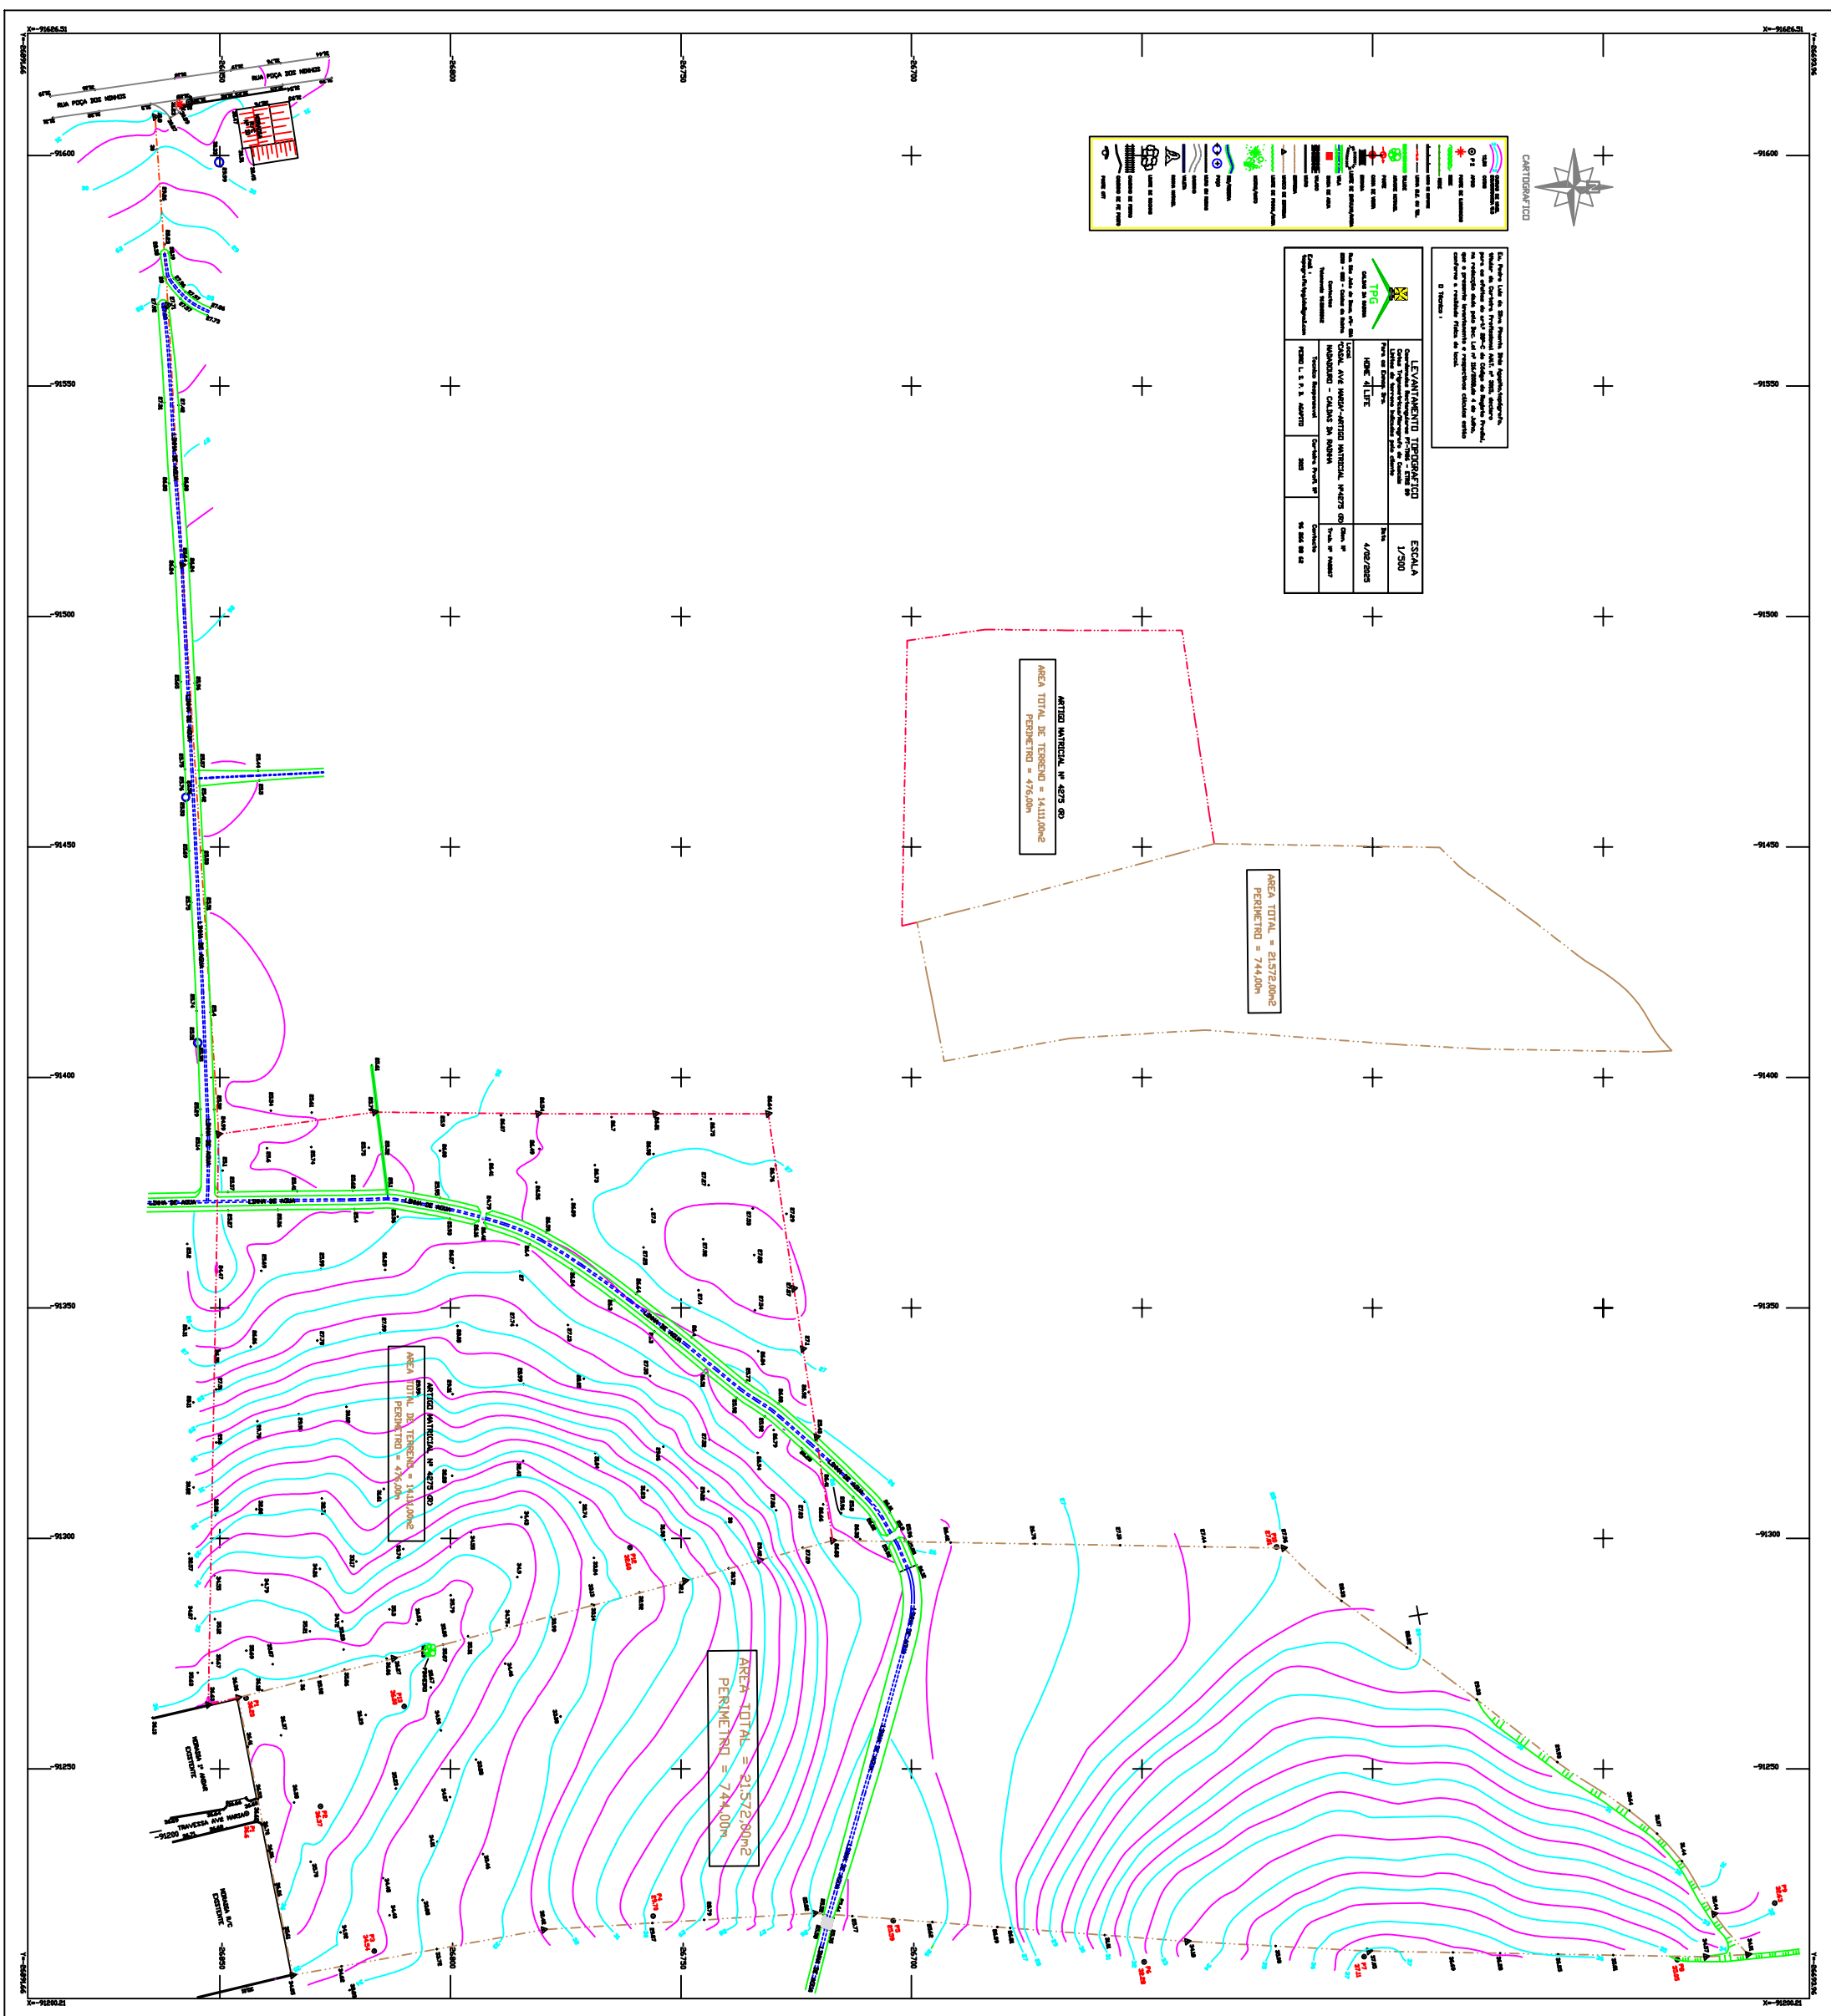

Para os devidos efeitos declara-se que a Ageas Portugal - Companhia de Seguros, S.A., designada por Ageas Portugal, com sede social em Praça Príncipe Perfeito 2, 1990-278 Lisboa, com o NIPC 503 454 109, celebrou um contrato de seguro de Responsabilidade Civil Profissional com a Ordem dos Arquitectos nas seguintes condições:

- N.º de Apólice: 008410215055
- Capital Seguro: 50.000 €
- Âmbito Territorial: Portugal Continental e Regiões Autónomas dos Açores e da Madeira.
- Franquia: 10% dos prejuízos indemnizáveis, num mínimo de 500 €
- Data início e fim do seguro: 01 de janeiro de 2026 a 31 de dezembro de 2026
- N.º Membro: 18423
- Nome Membro: João Carlos Fonseca Jorge

Esta declaração de seguro é emitida nos termos previstos nas Condições Gerais, Especiais e Particulares.

Data: Lisboa, 07 de Janeiro de 2026

Pela Ageas Portugal,



Luis Neves

Produção



Marisa Castro

Operações

CERTIDÃO PROFISSIONAL


CÓDIGO DE AUTENTICAÇÃO	NÚMERO	EMIÇÃO	VALIDADE
DC2C02085D637	3024/2026	07-01-2026	31-12-2026

A Ordem dos Arquitectos, associação pública profissional, ao abrigo do Estatuto da Ordem dos Arquitectos aprovado pelo Decreto-Lei n.º 176/98, de 3 de julho, na sua redação atual, certifica que:



João Carlos Fonseca Jorge, com o número de identificação civil **10749692**, é membro efetivo desta Ordem Profissional desde **10/03/2010**, com o número **18423**, encontrando-se com a inscrição em vigor e no pleno exercício dos seus direitos para a prática dos atos da profissão de arquiteto.

Nos termos previstos na Lei n.º 31/2009, de 3 de julho, na sua redação atual, e demais legislação aplicável, está ainda habilitado a exercer as funções:

Elaboração de Projetos de Engenharia Específicos - Espaços Exteriores - obras até à categoria III

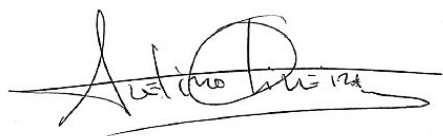

Avelino Oliveira, arquiteto
Presidente do Conselho Diretivo Nacional da Ordem dos Arquitectos

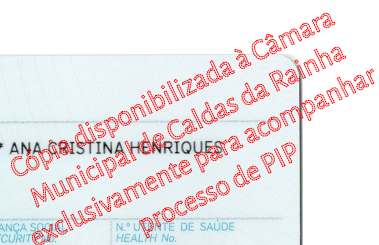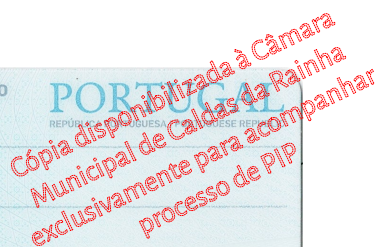

TERMO DE RESPONSABILIDADE DO AUTOR DO PROJECTO DE ARQUITECTURA

(conforme o anexo III da Portaria n.º 113/2015 de 22 de Abril)

26 de Janeiro de 2026

Da parte de: João Carlos Fonseca Jorge, que vive na Av. da Serrana, 4A, Serra d'El-Rei, beneficiário titular do documento de identificação n.º 10749692, e da inscrição na Ordem dos Arquitectos, com o n.º 18423, declara, para efeitos do disposto no n.º 1 do artigo 10.º do Decreto-Lei n.º 555/99, de 16 de Dezembro, na redacção que lhe foi conferida pelo Decreto-lei nº136/2014, de 9 de Setembro, que o projecto de Arquitectura, de que é autor, relativo ao Pedido de Informação Prévia de **Hotel Rural e Apoios para Agro-florestal**, localizado em Casal d'Avé Maria, Nadadouro, freguesia de União das freguesias de Caldas da Rainha – Santo Onofre e Serra do Bouro, concelho de Caldas da Rainha, requerido por **Robert Roztock**i, com direcção em Untere Roostmatt 8, 6300 Zug - Suíça, observa a legitimidade, as normas legais e regulamentares aplicáveis, designadamente, o Regime Jurídico da Urbanização e Edificação (RJUE) e está conforme com os planos municipais ou intermunicipais de ordenamento do território aplicáveis à pretensão, salvo melhor interpretação jurídica, não constituindo reconhecimento de factos ou qualificações jurídicas.

Técnico responsável

Por: João Jorge arq.º beneficiário OA n.º18423

Sob reserva de direitos

A assinatura digital aposta visa exclusivamente garantir a identificação do signatário e a integridade do documento, salvo melhor interpretação jurídica.

TERMO DE RESPONSABILIDADE DO COORDENADOR DO PROJECTO DE ARQUITECTURA

(conforme o anexo III da Portaria n.º 113/2015 de 22 de Abril)

26 de Janeiro de 2026

Da parte de: João Carlos Fonseca Jorge, que vive na Av. da Serrana, 4A, Serra d'El-Rei, beneficiário titular do documento de identificação n.º 10749692, e da inscrição na Ordem dos Arquitectos, com o número 18423, declara, para efeitos do disposto no n.º 1 do artigo 10.º do Decreto-Lei n.º 555/99, de 16 de Dezembro, na redacção que lhe foi conferida pelo Decreto-lei nº136/2014, de 9 de Setembro, que o projecto de Arquitectura, de que é autor, relativo ao Pedido de Informação Prévia de **Hotel Rural e Apoios para Agro-florestal**, localizado em Casal d'Avé Maria, Nadadouro, freguesia de União das freguesias de Caldas da Rainha – Santo Onofre e Serra do Bouro, concelho de Caldas da Rainha, requerido por **Robert Roztock**, com direcção em Untere Roostmatt 8, 6300 Zug - Suíça, observa a legitimidade, as normas legais e regulamentares aplicáveis, designadamente, o Regime Jurídico da Urbanização e Edificação (RJUE) e está conforme com os planos municipais ou intermunicipais de ordenamento do território aplicáveis à pretensão, salvo melhor interpretação jurídica, não constituindo reconhecimento de factos ou qualificações jurídicas.

Técnico responsável

Por: João Jorge arq.º beneficiário OA n.º18423

Sob reserva de direitos

A assinatura digital aposta visa exclusivamente garantir a identificação do signatário e a integridade do documento, salvo melhor interpretação jurídica.

Nº. Processo: 3769826 Data de Entrada: 26/09/2025 10:54:55 Validado por: celina.r.almeida

Dados do Prédio

Concelho	Freguesia	Natureza	Nº. Matriz	Árvore/Colonia
Caldas da Rainha	Caldas da Rainha - Santo Onofre e Serra do Bouro	Rústico	3978	-

Dados da Pessoa

Nome	Identificação	Qualidade
HOME 4 LIFE LDA	513229477	Representado, Titular
Norberto da Conceição Dimas Pereira Henriques	168992477	Promotor, Representante

Representação Gráfica Georreferenciada (RGG)**Área**
23583.00 m²**Coordenadas do Centroide**
Oficiais ETRS89 PT-TM06 (M,P): -91257.4361, -26707.4998
Geográficas WGS84 (Lat, Long): 39.42287872, -9.19289367

Norberto da Conceição Dimas Pereira Henriques, na qualidade de promotor/proprietário e representante de HOME 4 LIFE LDA, declara serem da sua inteira responsabilidade os dados relativos à delimitação do polígono constante da RGG do processo nº 3769826.

Mais declara que autoriza que os seus dados pessoais, constantes do presente procedimento de RGG, sejam utilizados para efeitos de notificação no âmbito do procedimento de conciliação administrativa.

26-09-2025 11:13:54
Assinatura